ОБЩЕСТВО С ОГРАНИЧЕННОЙ ОТВЕТСТВЕННОСТЬЮ
«СЕНАТОР ТЕЛЕКОМ»
199106, г. Санкт-Петербург, Большой пр. В.О., д. 80 лит.А офис 34-Н, тел. 332-1700, факс 332-1213

по адресу : Санкт-Петербург, ул. Чапаева,д.15, корпус Ж, 4 этаж

Исполнительная документация
Структурированная кабельная система

Ч15-Ж-2021-СКС

Санкт-Петербург
2021 г.

Ведомость документов основного комплекта

Лист	Наименование	Примечание
1	Общие данные	на 2 листах
2.1	План расположения кабельных линий и портов СКС	на 1 листе
2.2	План расположения портов и кабельных линий	на 1 листе
3	Фасад телекоммуникационного шкафа ТШ-1	на 1 листе
4.1-4.2	Схема расключения кабельных линий на патч-панелях в ТШ-1	на 2 листах

Согласовано

Взам. инв. №

Подп. и дата

Инв. № подл.

Изм.	Кол.уч.	Лист	№док.	Подп.	Дата	Ч15-Ж-2021-СКС		
Разраб.		Епифанов			03.21	Общие данные	Стадия	Лист	Листов
ГИП		Бурлаков			03.21		И	1.1	2
							ООО «СЕНАТОР ТЕЛЕКОМ»		

Ведомость ссылочных и прилагаемых документов

Обозначение	Наименование	Примечание
	Ссылочные документы	
Постановление правительства РФ от 16.02.08 г. №87	О составе разделов проектной документации и требования к их содержанию	
ГОСТ Р 21.1101-2013	Основные требования к проектной и рабочей документации	
ГОСТ Р 53246-2008	Информационные технологии. Системы кабельные структурированные. Проектирование основных узлов системы. Общие требования	
TIA-942	Телекоммуникационная инфраструктура Центров Обработки Данных	

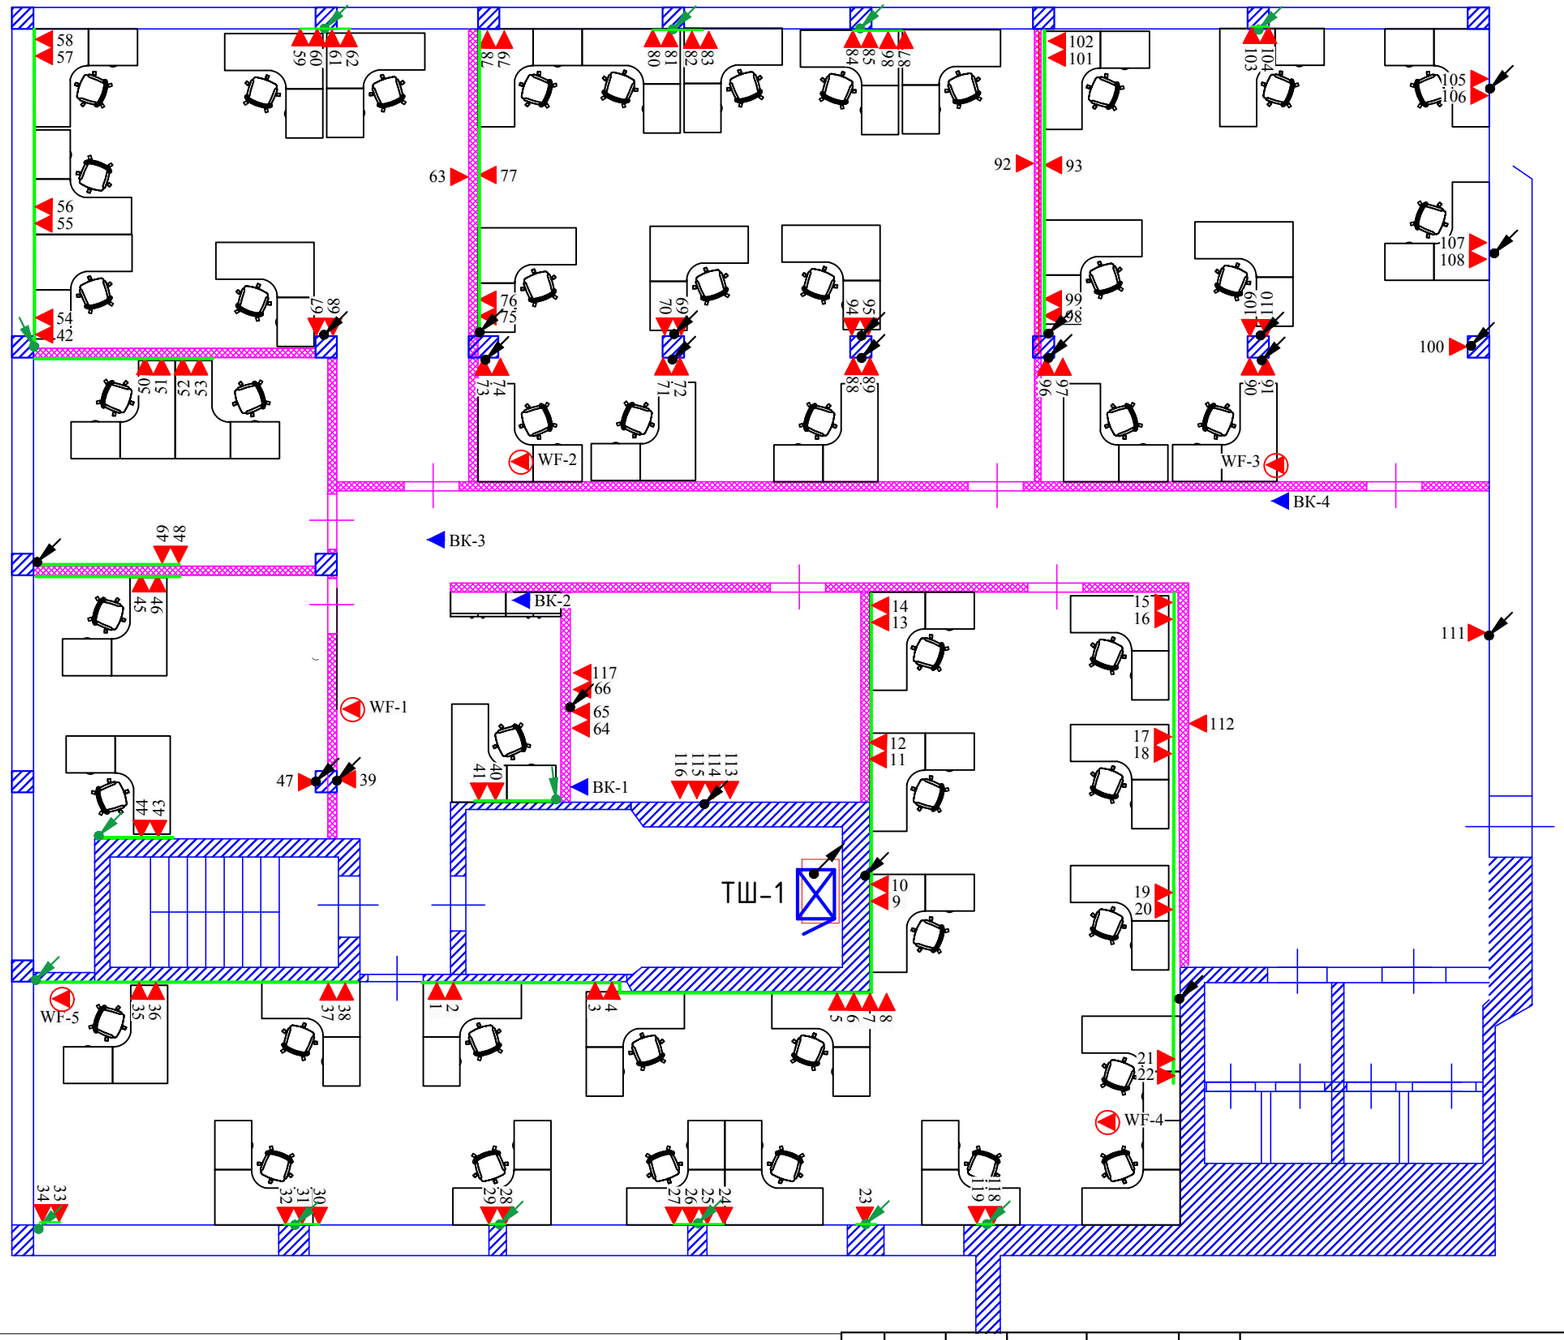

УСЛОВНЫЕ ОБОЗНАЧЕНИЯ:

- *Розетка RJ-45 кат. 5е в кабель-канале*
- *Розетка RJ-45 кат. 5е в ГКЛ*
- *Кабель обжат вилкой RJ-45 кат.5е за потолком. для Wi-Fi. запас 3 м.*
- *Кабель обжат вилкой RJ-45 кат.5е за потолком. Для СВН. Запас 3 м.*
- *Кабель UTP кат.5е проложен за потолком в гофротрубе*
- *Кабель UTP кат.5е проложен в кабель-канале DLP 105x50. (крепление кабель-канала к полу на двухстороннюю клейкую ленту)*
- *Опуск/ подъем кабеля*
- *Опуск кабеля в кабель-канале*
- *Телекоммуникационный шкаф 600x1000 42U*

Взам. инв. №	Подпись и дата	Инв. № подл.

Изм	Кол.уч	Лист	№ Док.	Подпись	Дата	Ч15-Ж-2021-СКС		
						г.Санкт-Петербург, ул.Чапаева, д.15., лит.Ж, 4 эт.		
ГИП		Бурлаков			03.21	Структурированная кабельная система	Стадия	Лист	Листов
							И	2.1	2
Разраб.		Епифанов			03.21	Схема расположения портов СКС	ООО "Сенатор Телеком"		

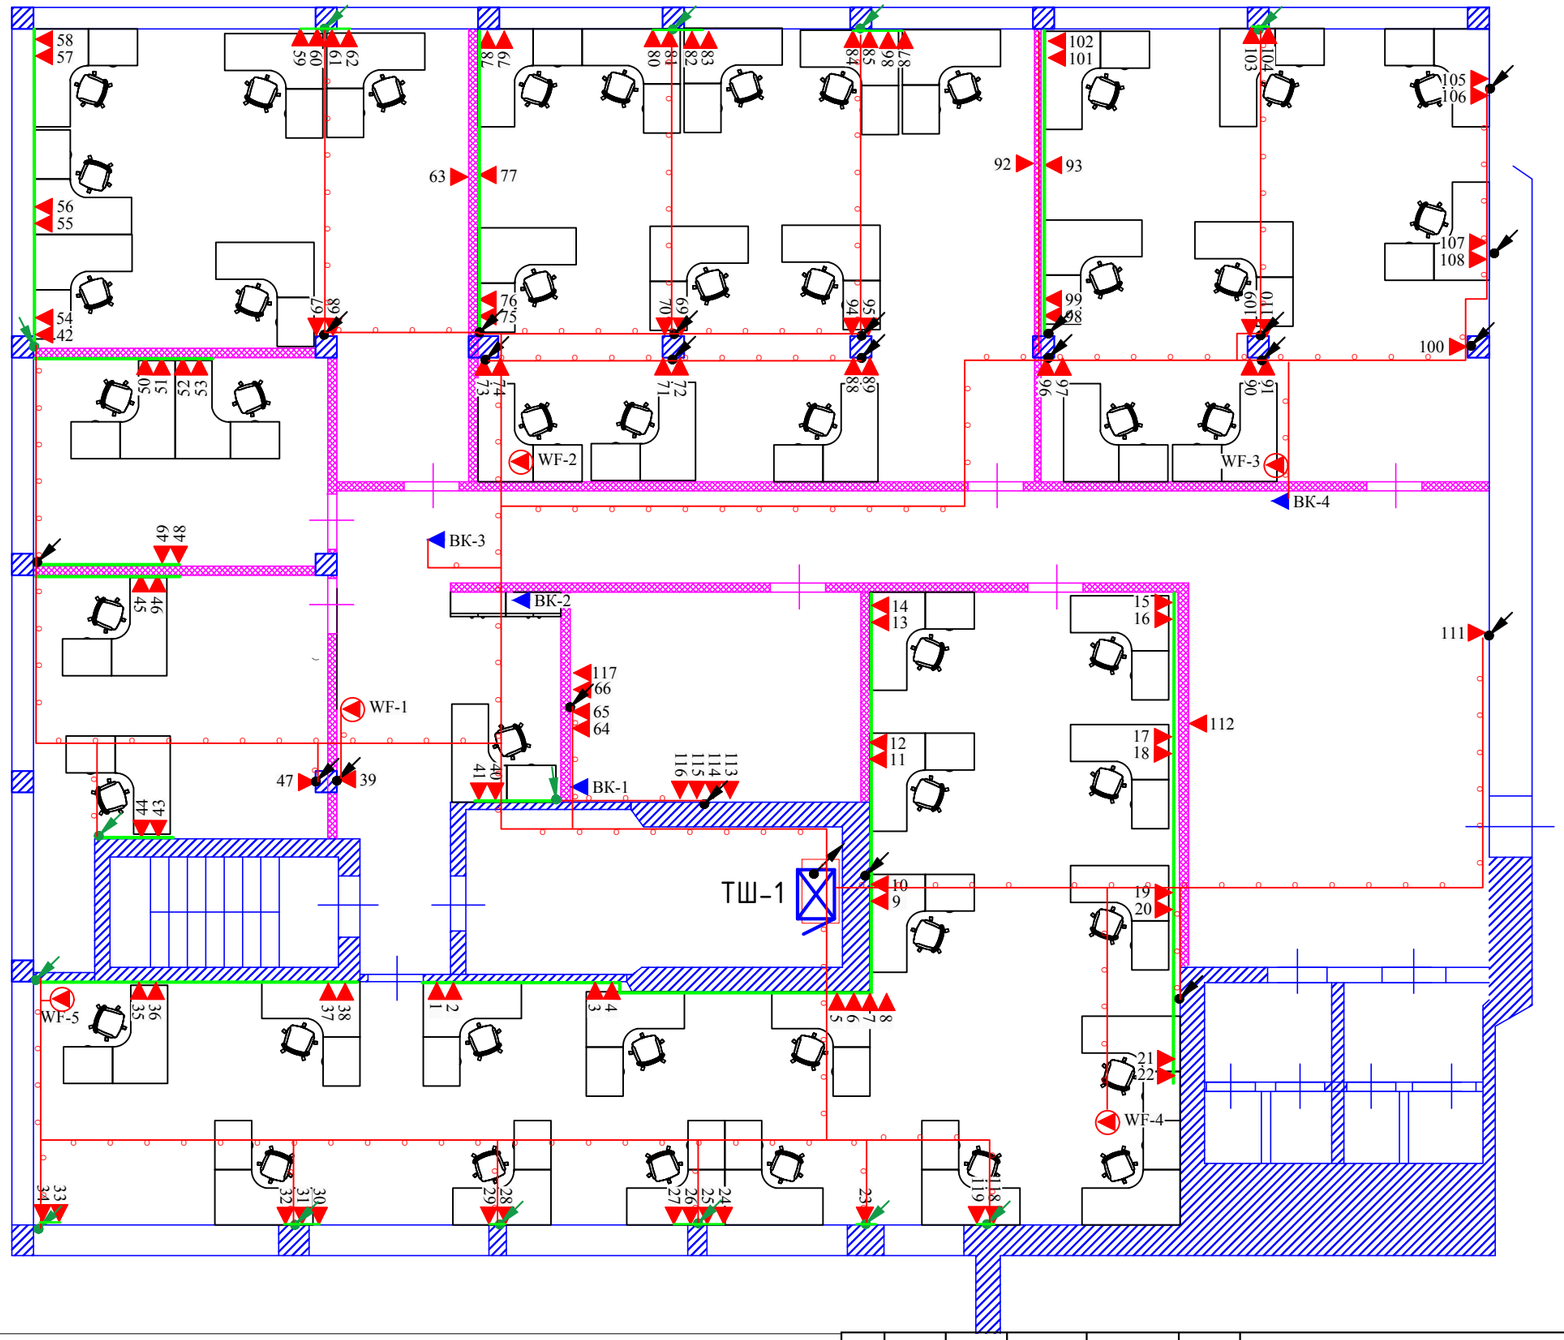

УСЛОВНЫЕ ОБОЗНАЧЕНИЯ:

- *Розетка RJ-45 кат. 5е в кабель-канале*
- *Розетка RJ-45 кат. 5е в ГКЛ*
- *Кабель обжат вилкой RJ-45 кат.5е за потолком. для Wi-Fi. запас 3 м.*
- *Кабель обжат вилкой RJ-45 кат.5е за потолком. Для СВН. Запас 3 м.*
- *Кабель UTP кат.5е проложен за потолком в гофротрубе*
- *Кабель UTP кат.5е проложен в кабель-канале DLP 105x50. (крепление кабель-канала к полу на двухстороннюю клейкую ленту)*
- *Опуск/ подъем кабеля*
- *Опуск кабеля в кабель-канале*
- *Телекоммуникационный шкаф 600x1000 42U*

Взам. инв. №	Подпись и дата	Инв. № подл.

Изм	Кол.уч	Лист	№ Док.	Подпись	Дата	Ч15-Ж-2021-СКС		
						г.Санкт-Петербург, ул.Чапаева, д.15., лит.Ж, 4 эт.		
ГИП		Бурлаков			03.21	Структурированная кабельная система	Стадия	Лист	Листов
							И	2.2	2
Разраб.		Епифанов			03.21	Схема расположения кабельных линий и портов СКС	ООО "Сенатор Телеком"		

ТШ-1

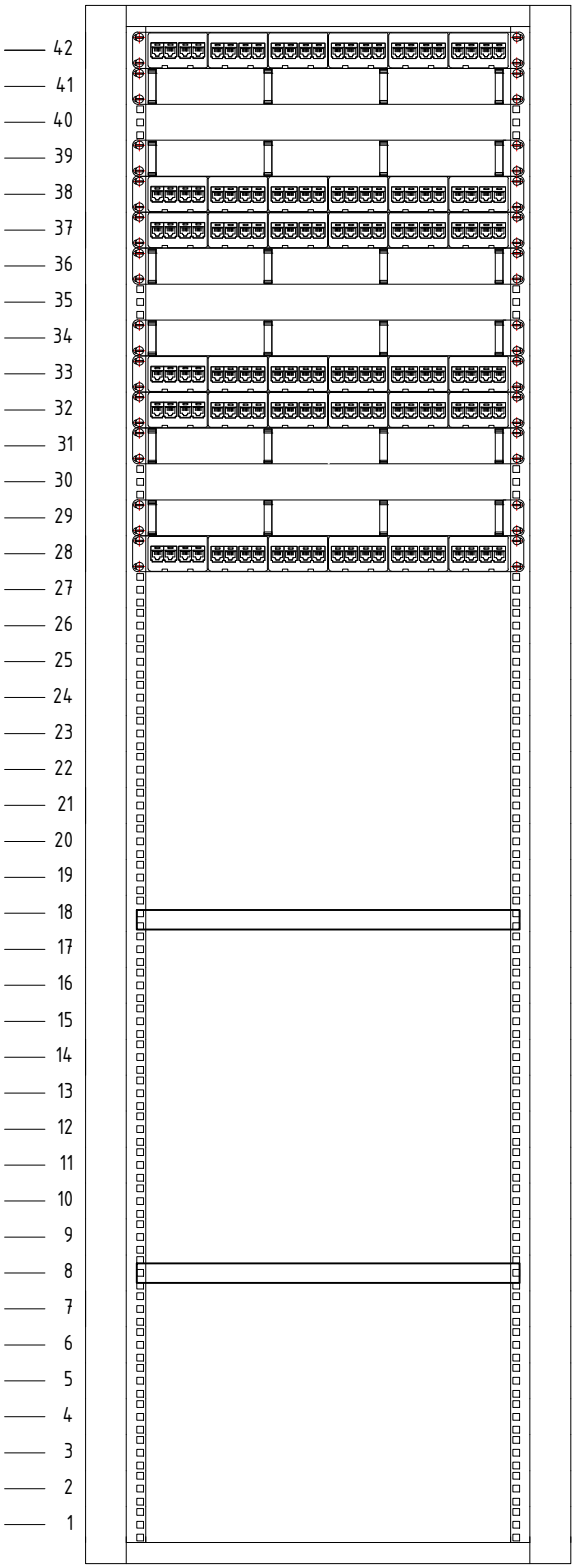

Unit	Маркировка	Наименование
42	П.П.-1	Патч-панель 24 порта кат.5е
41		Организатор
40		Коммутатор 48 портов
39		Организатор
38	П.П.-2	Патч-панель 24 порта кат.5е
37	П.П.-3	Патч-панель 24 порта кат.5е
36		Организатор
35		Коммутатор 48 портов
34		Организатор
33	П.П.-4	Патч-панель 24 порта кат.5е
32	П.П.-5	Патч-панель 24 порта кат.5е
31		Организатор
30		Коммутатор 48 портов
29		Организатор
28	П.П.-6	Патч-панель 24 порта кат.5е
27		
26		
25		
24		
23		
22		
21		
20		
19		
18		Полка для оборудования
17		
16		
15		
14		
13		
12		
11		
10		
9		
8		Полка для оборудования
7		
6		
5		
4		
3		
2		
1		

Взам. инв. №

Подпись и дата

Инв. № подл.

Изм	Кол.уч	Лист	№ Док.	Подпись	Дата
ГИП		Бурлаков			03.21
Разраб.		Епифанов			03.21

Ч15-Ж-2021-СКС

г.Санкт-Петербург, ул.Чапаева, д.15., лит.Ж, 4 эт.

Структурированная кабельная система

Стадия	Лист	Листов
И	3	1

Фасад телекоммуникационного шкафа ТШ-1

ООО "Сенатор Телеком"

	Телеком распред	Марк. панели	Тип	Прим ечч.		
Откуда:	ТШ-1	П.П.-1	24 порта RJ-45, 4-пары		№ порта	1 2 3 4 5 6 7 8 9 10 11 12 13 14 15 16 17 18 19 20 21 22 23 24
					Маркировка розетки	1 2 3 4 5 6 7 8 9 10 11 12 13 14 15 16 17 18 19 20 21 22 23 24
					Тип кабеля	UTP Cat.5e 4pair
Куда:	рабочие места					

	Телеком распред	Марк. панели	Тип	Прим ечч.		
Откуда:	ТШ-1	П.П.-2	24 порта RJ-45, 4-пары		№ порта	1 2 3 4 5 6 7 8 9 10 11 12 13 14 15 16 17 18 19 20 21 22 23 24
					Маркировка розетки	25 26 27 28 29 30 31 32 33 34 35 36 37 38 39 40 41 42 43 44 45 46 47 48
					Тип кабеля	UTP Cat.5e 4pair
Куда:	рабочие места					

	Телеком распред	Марк. панели	Тип	Прим ечч.		
Откуда:	ТШ-1	П.П.-3	24 порта RJ-45, 4-пары		№ порта	1 2 3 4 5 6 7 8 9 10 11 12 13 14 15 16 17 18 19 20 21 22 23 24
					Маркировка розетки	49 50 51 52 53 54 55 56 57 58 59 60 61 62 63 64 65 66 67 68 69 70 71 72
					Тип кабеля	UTP Cat.5e 4pair
Куда:	рабочие места					

	Телеком распред	Марк. панели	Тип	Прим ечч.		
Откуда:	ТШ-1	П.П.-4	24 порта RJ-45, 4-пары		№ порта	1 2 3 4 5 6 7 8 9 10 11 12 13 14 15 16 17 18 19 20 21 22 23 24
					Маркировка розетки	73 74 75 76 77 78 79 80 81 82 83 84 85 86 87 88 89 90 91 92 93 94 95 96
					Тип кабеля	UTP Cat.5e 4pair
Куда:	рабочие места					

Взам. инв. №

Подпись и дата

Инв. № подл.

Изм	Кол.уч	Лист	№ Док.	Подпись	Дата
ГИП		Бурлаков			03.21
Разраб.		Епифанов			03.21

Ч15-Ж-2021-СКС

г.Санкт-Петербург, ул.Чапаева, д.15., лит.Ж, 4 эт.

Структурированная кабельная система

Стадия	Лист	Листов
И	4.1	2

Фасад телекоммуникационного шкафа ТШ-1

ООО "Сенатор Телеком"

	Телеком распред	Марк. панели	Тип	Прим ечч.																							
Откуда:	ТШ-1	П.П.-5	24 порта RJ-45, 4-пары		№ порта	1	2	3	4	5	6	7	8	9	10	11	12	13	14	15	16	17	18	19	20	21	22	23	24
					Маркировка розетки	97	98	99	100	101	102	103	104	105	106	107	108	109	110	111	112	113	114	115	116	117	118	119	
					Тип кабеля	UTP Cat.5e 4pair																							
Куда:	рабочие места																												

	Телеком распред	Марк. панели	Тип	Прим ечч.																							
Откуда:	ТШ-1	П.П.-6	24 порта RJ-45, 4-пары		№ порта	1	2	3	4	5	6	7	8	9	10	11	12	13	14	15	16	17	18	19	20	21	22	23	24
					Маркировка розетки	WF-1	WF-2	WF-3	WF-4	WF-5	BK-1	BK-2	BK-3	BK-4															
					Тип кабеля	UTP Cat.5e 4pair																							
Куда:	рабочие места																												

Взам. инв. №	Подпись и дата	Инв. № подл.

Изм	Кол.уч	Лист	№ Док.	Подпись	Дата

Ч15-Ж-2021-СКС

Лист 4.2