офисные помещения Первомайская 21

1 этаж

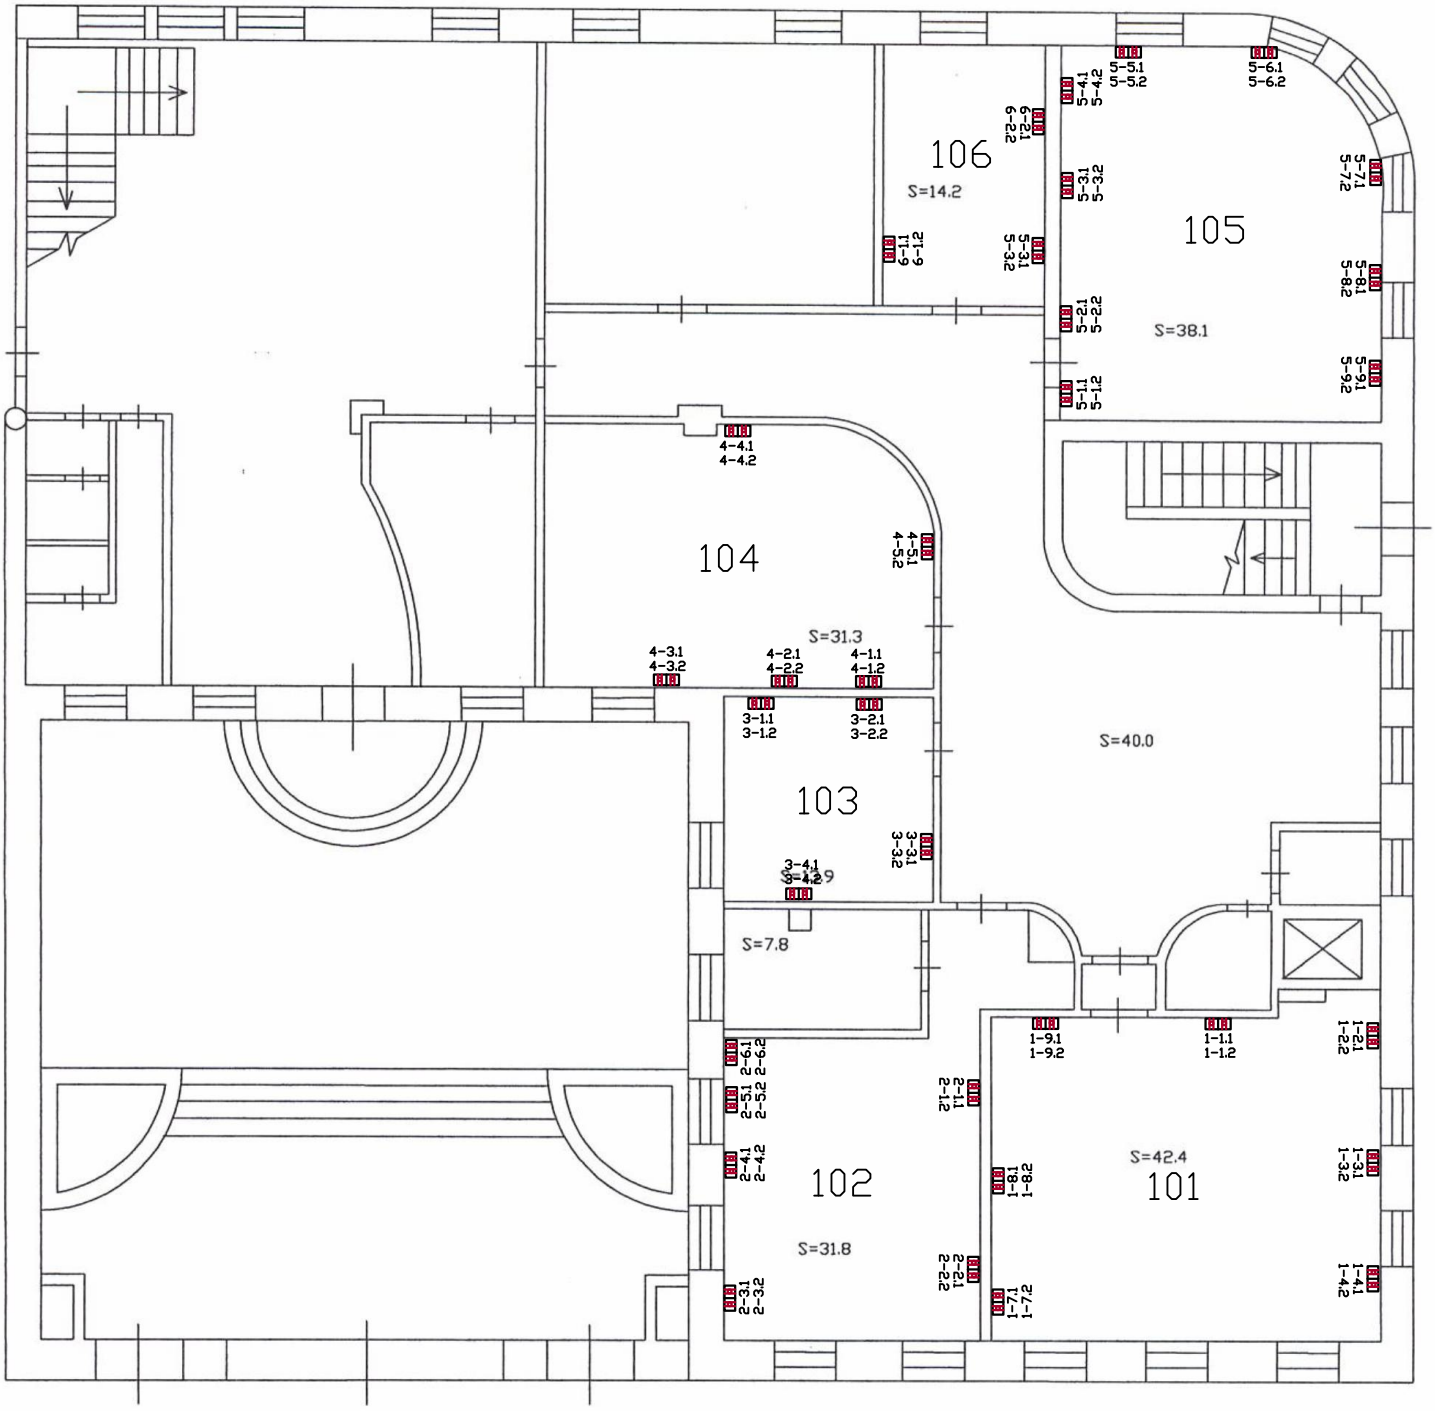


Общая площадь помещений-528.4 м2

Площадь кабинетов-366.0 м2

Площадь МОП-92.9 м2

Площадь архива-69.5 м2