офисные помещения Первомайская 19
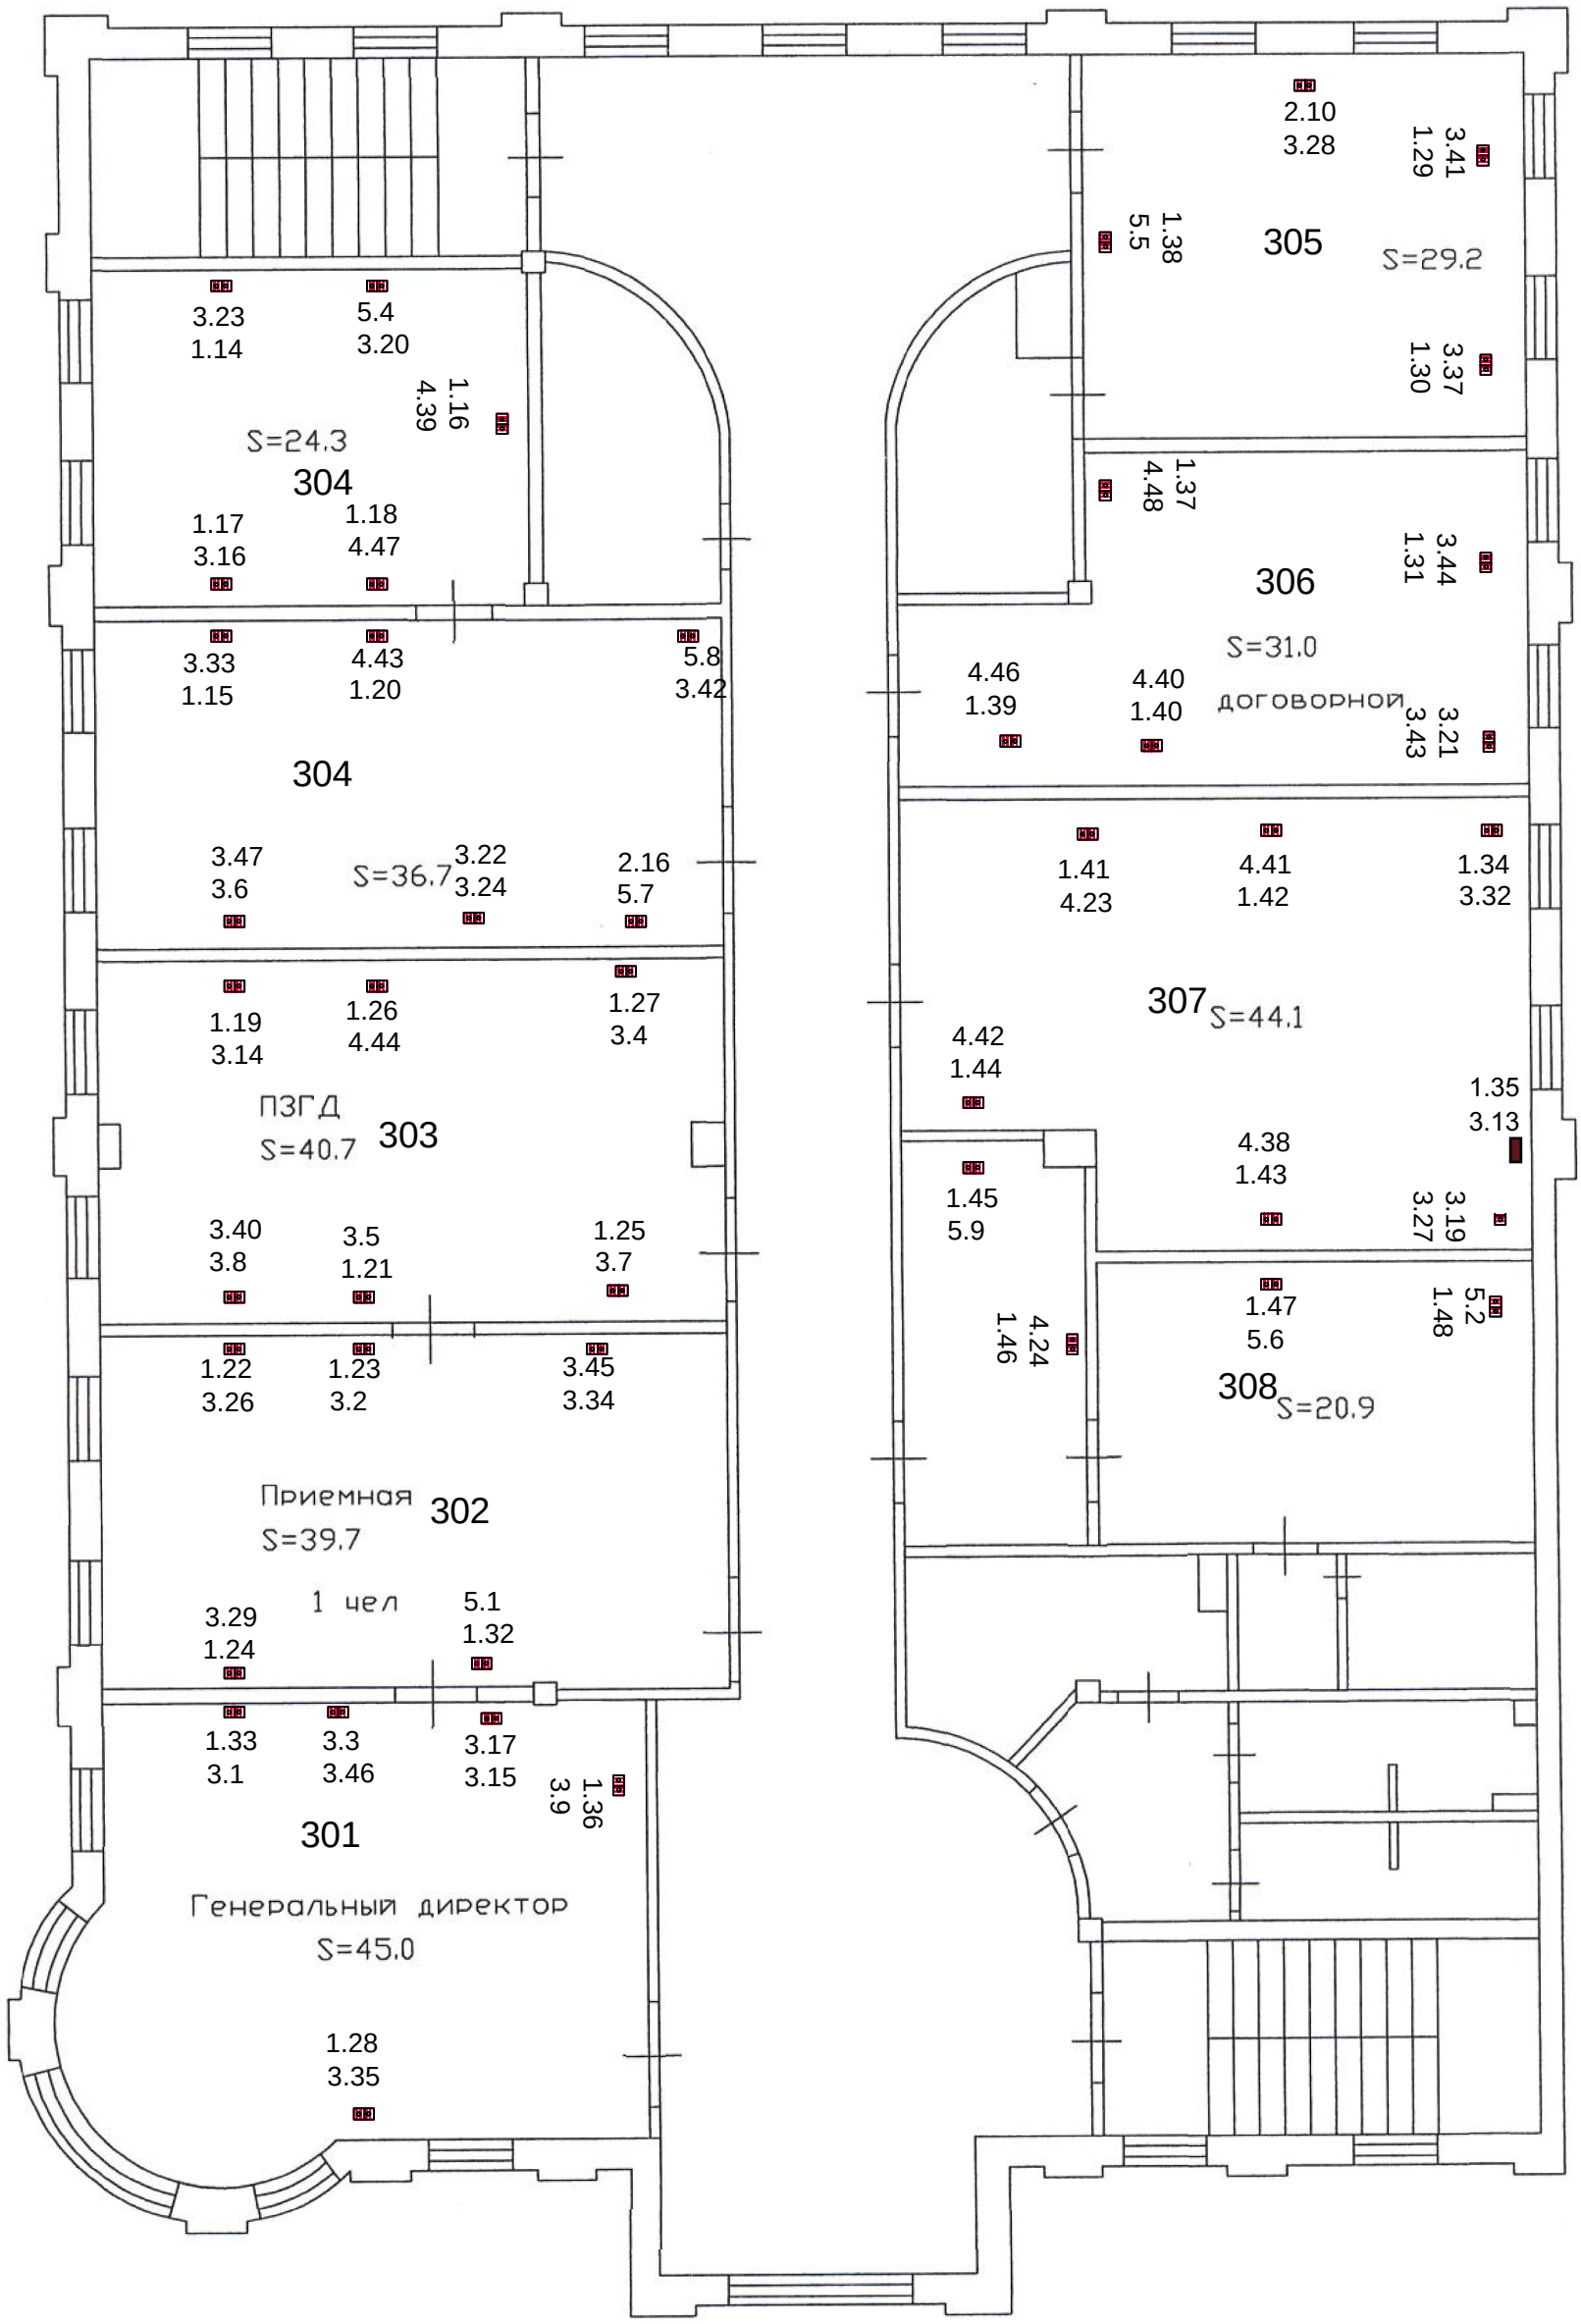
3-этаж