офисные помещения Первомайская 19
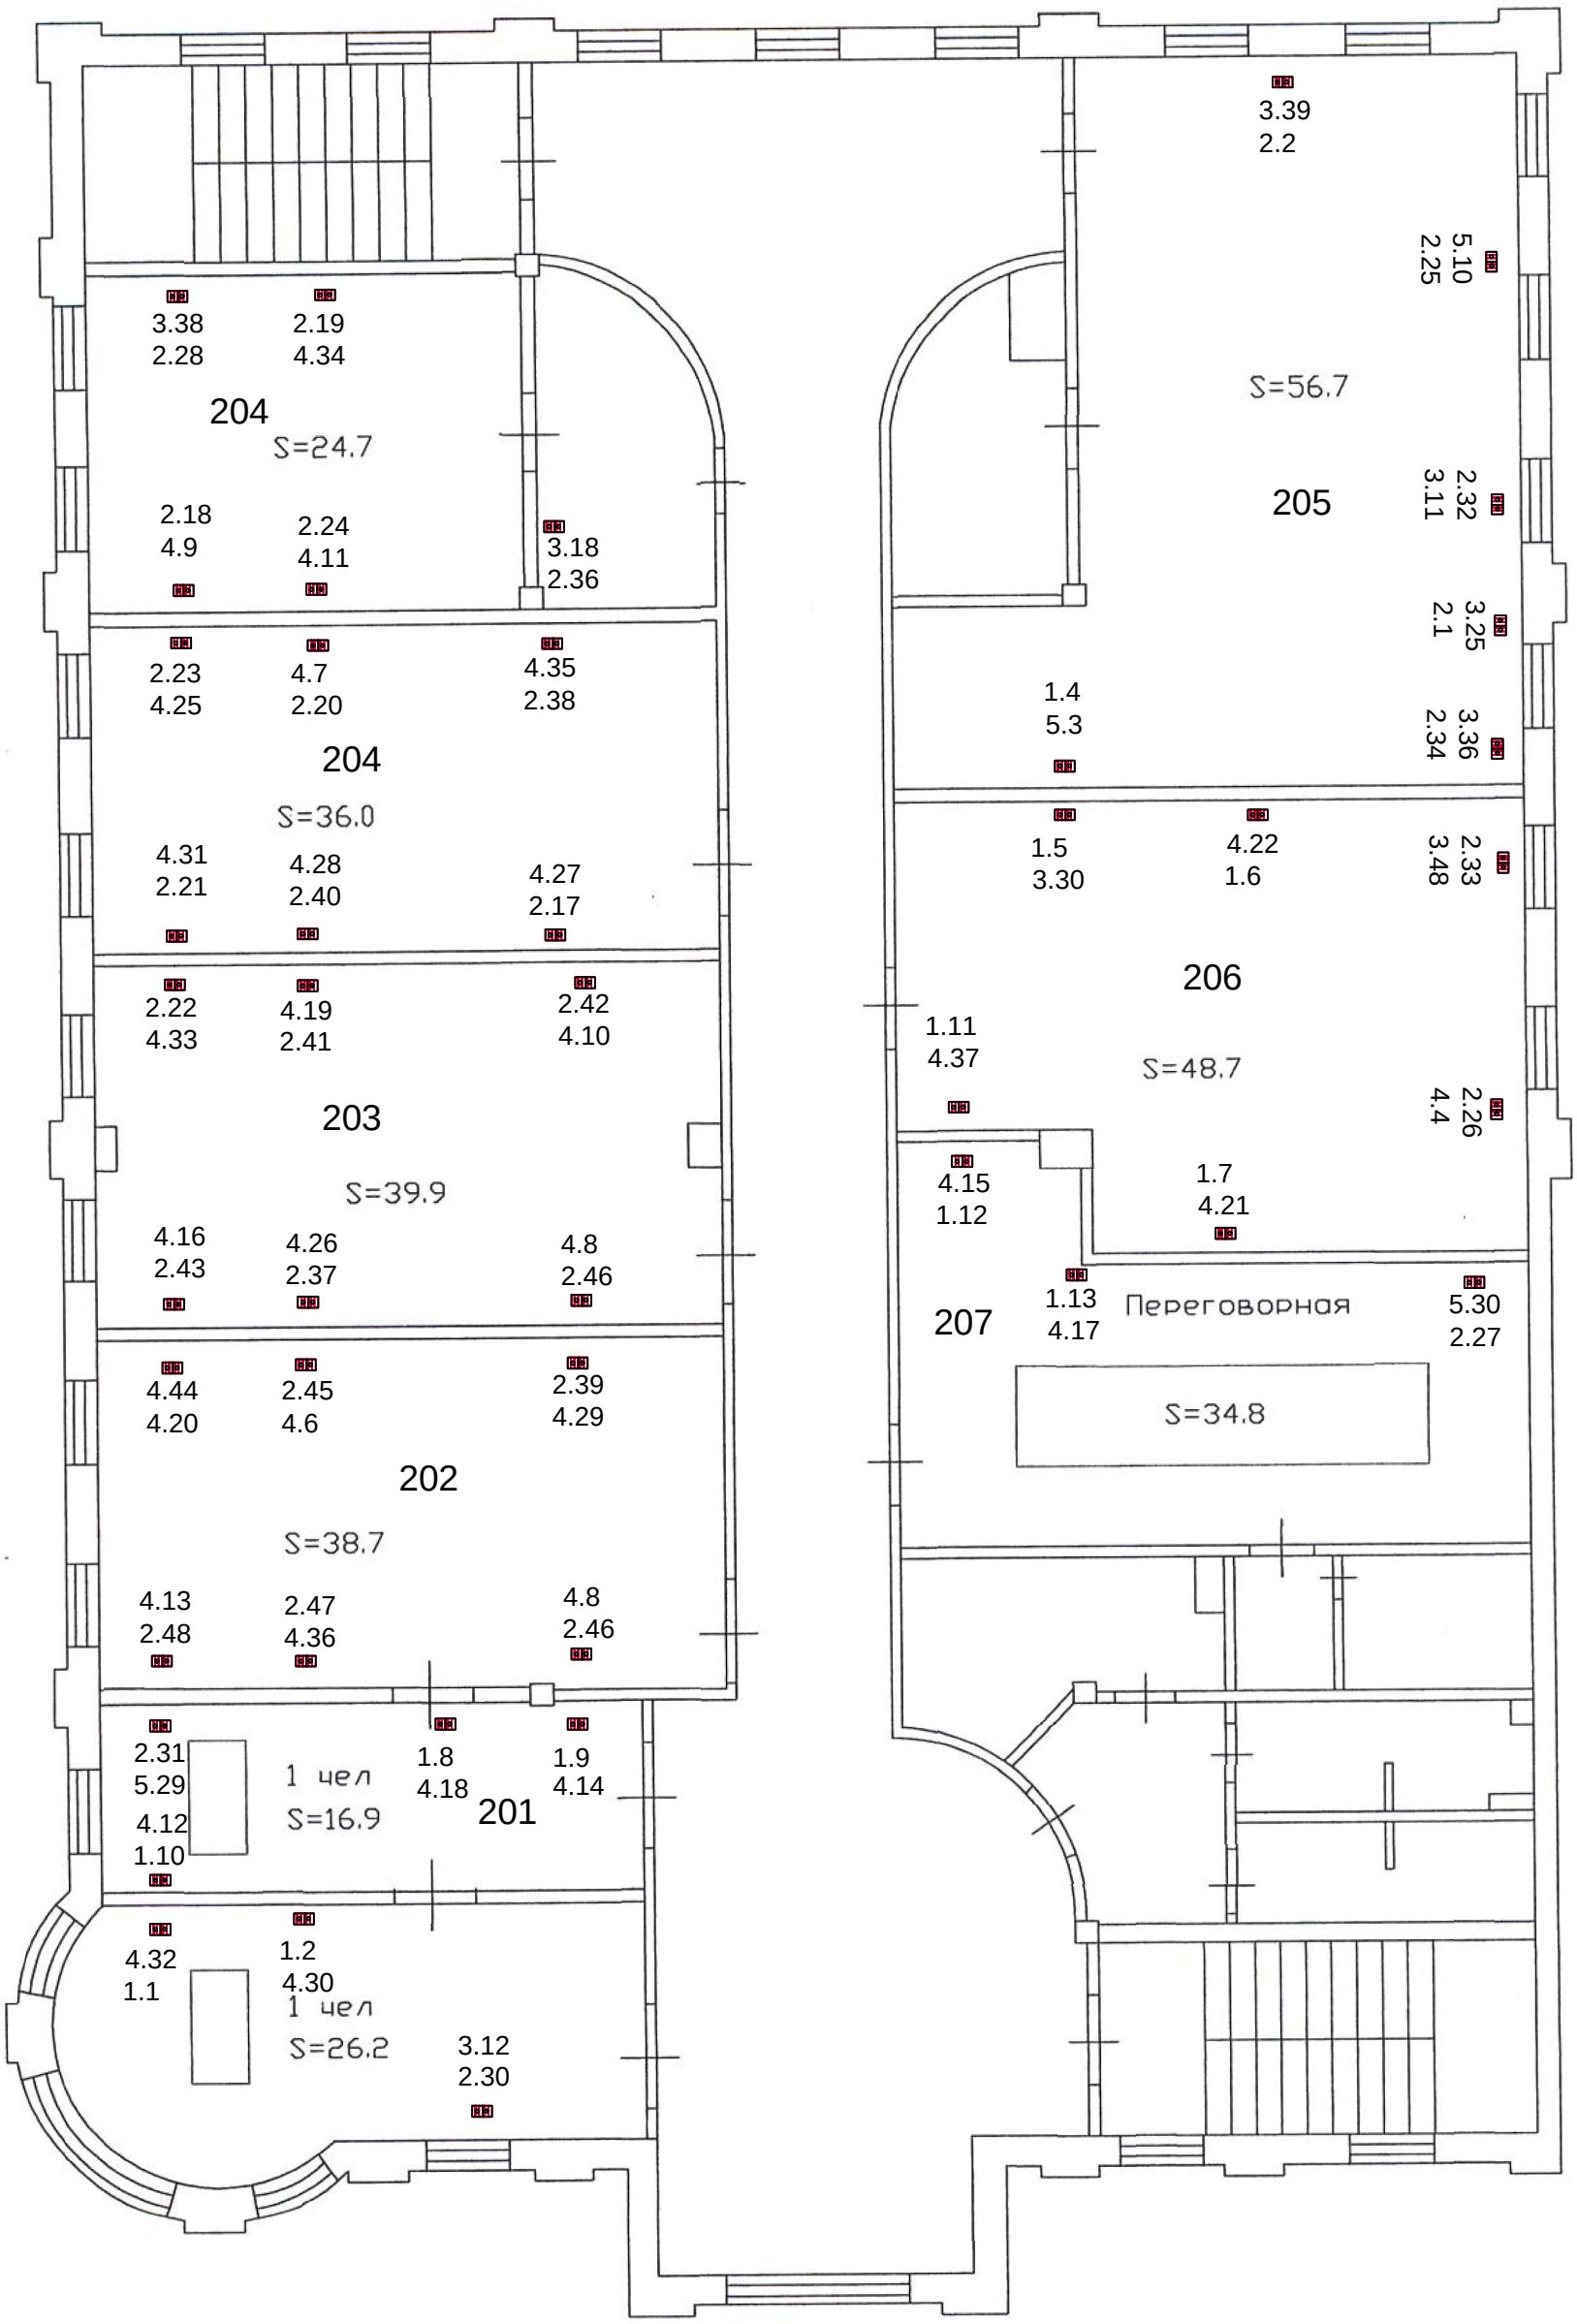
2-этаж