План 1

этажа

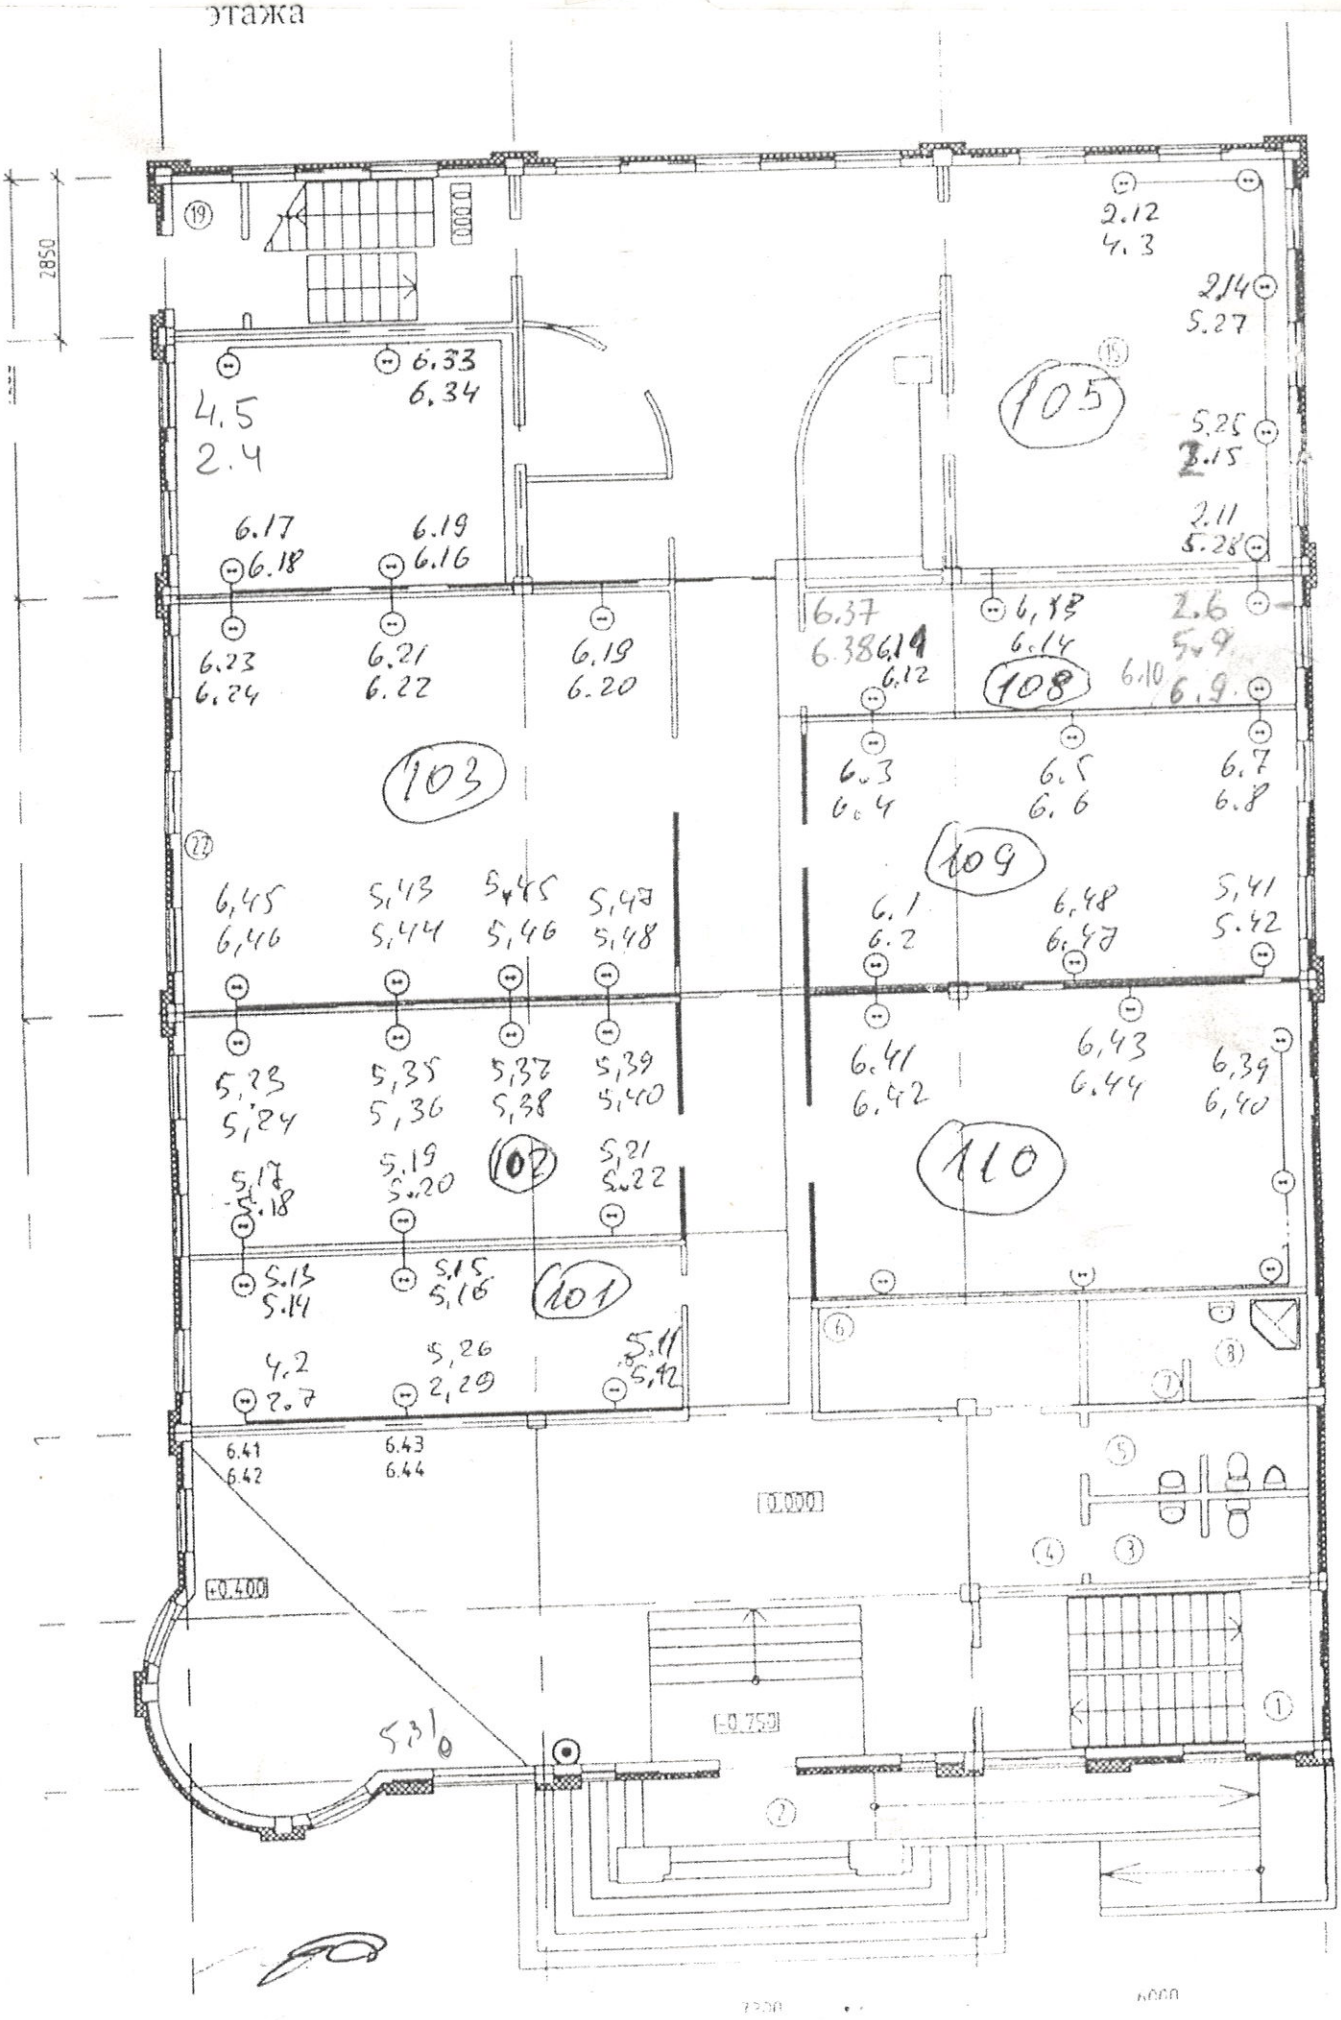

План 2 этажа

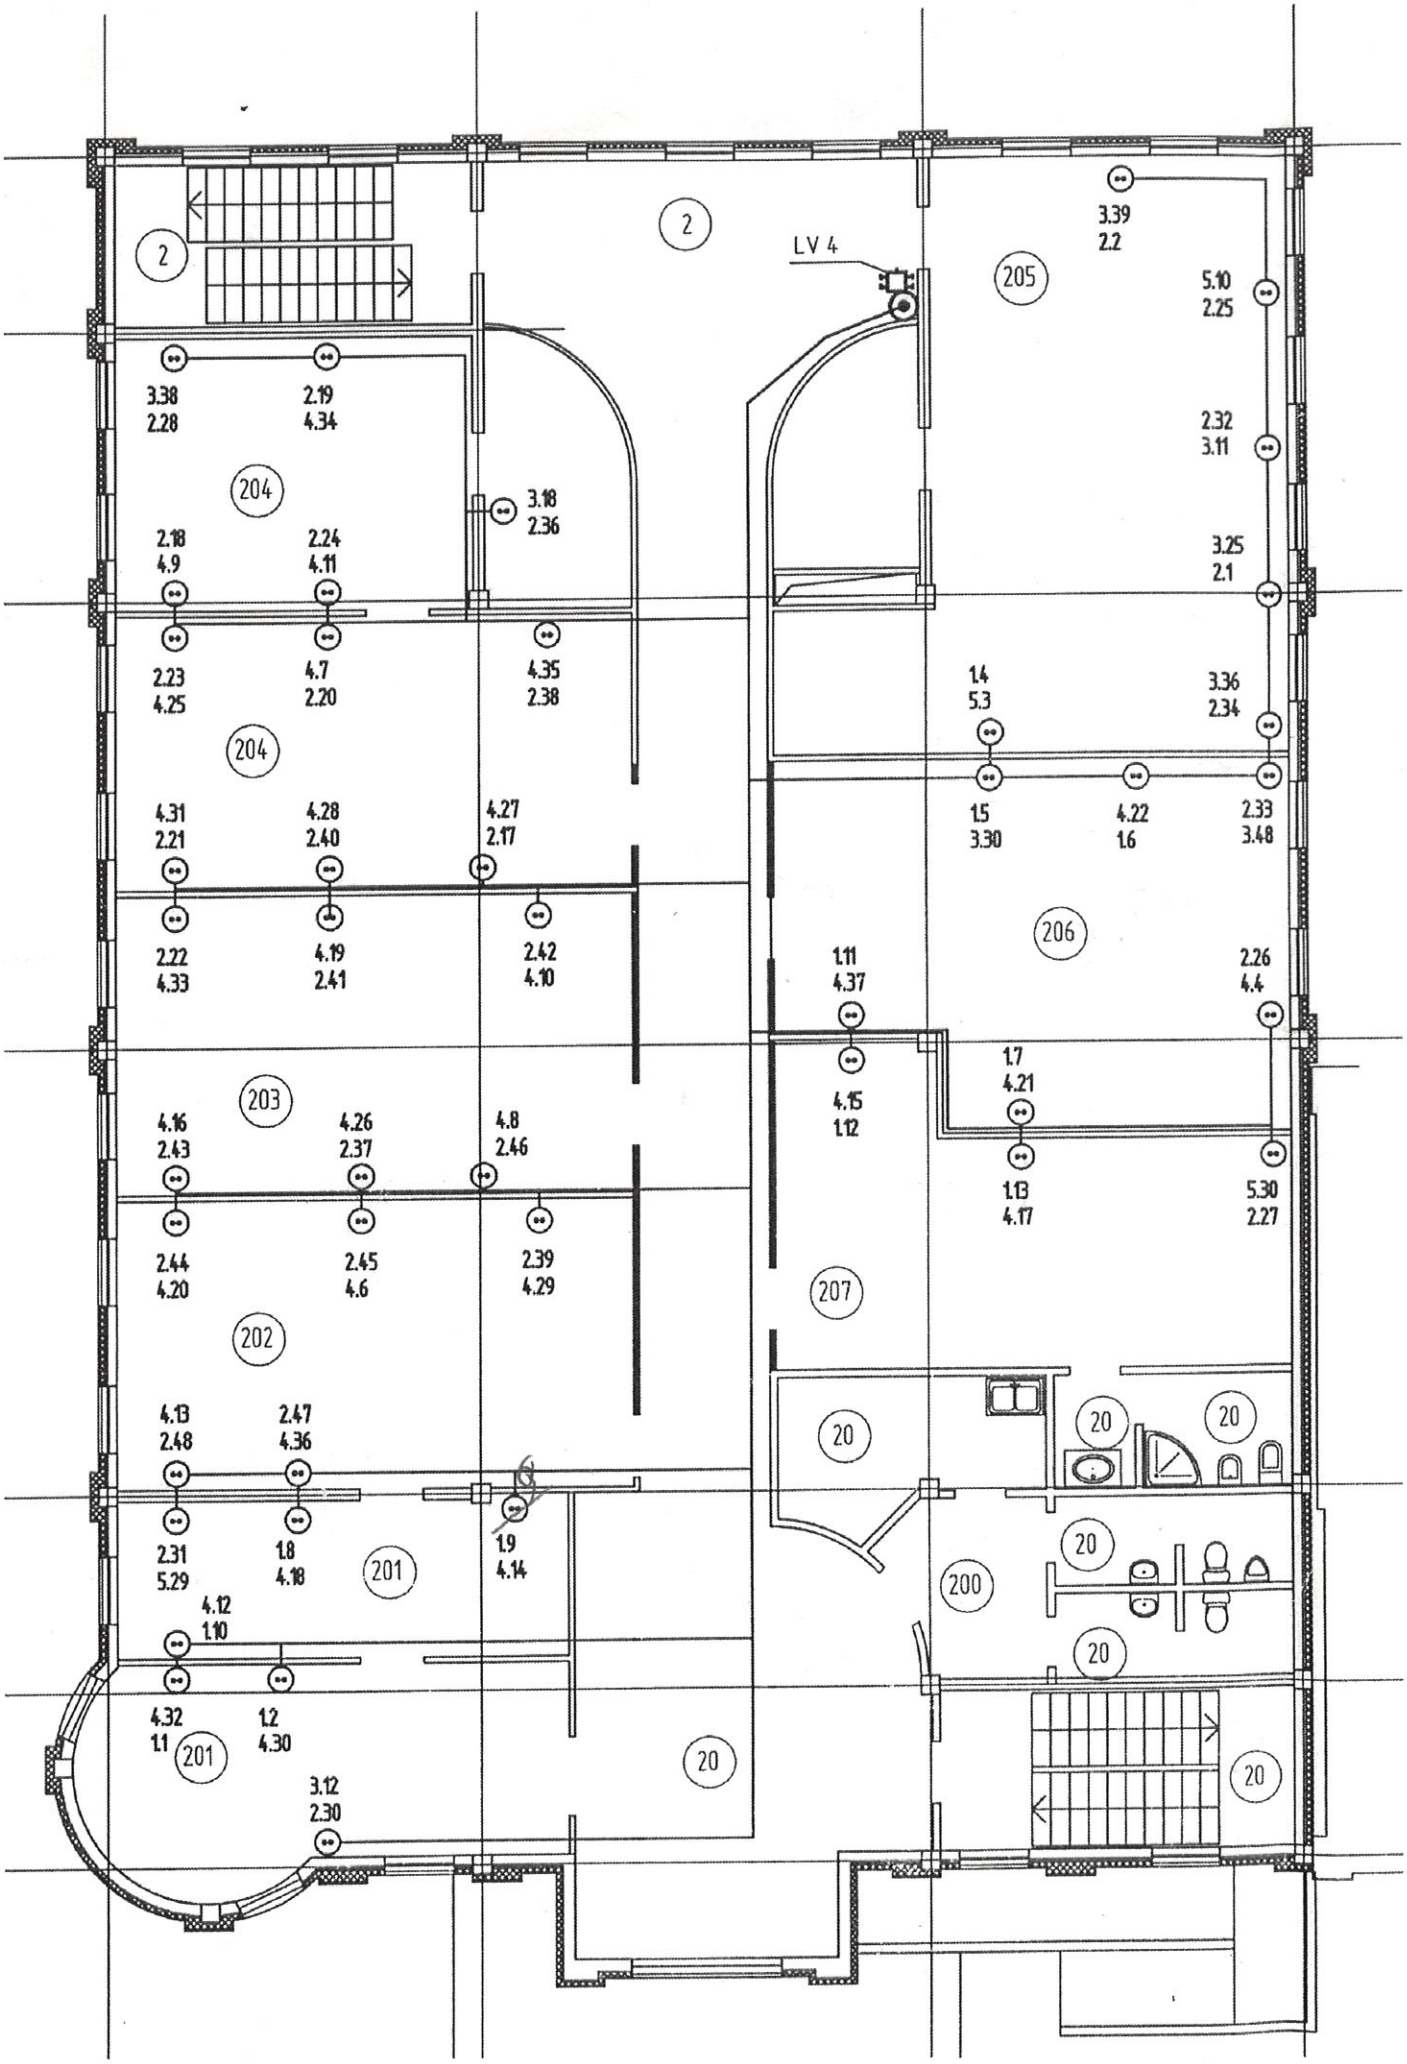
2
2
LV 4
205
3.39
2.2
5.10
2.25
3.38
2.28
2.19
4.34
204
3.18
2.36
2.32
3.11
2.18
4.9
2.24
4.11
3.25
2.1
2.23
4.25
4.7
2.20
4.35
2.38
204
1.4
5.3
3.36
2.34
1.5
3.30
4.22
1.6
2.33
3.48
4.31
2.21
4.28
2.40
4.27
2.17
2.22
4.33
4.19
2.41
2.42
4.10
206
1.11
4.37
2.26
4.4
1.7
4.21
4.15
1.12
203
4.16
2.43
4.26
2.37
4.8
2.46
1.13
4.17
5.30
2.27
2.44
4.20
2.45
4.6
2.39
4.29
207
202
20
20
20
4.13
2.48
2.47
4.36
2.31
5.29
1.8
4.18
1.9
4.14
201
200
20
4.12
1.10
20
4.32
1.1
1.2
4.30
201
20
20
3.12
2.30